


Location:
Japan

Architetti:
Kazuo Monnai
Hirokazu Ohara
Dai Tsunenobu
Kazuya Masui

Superficie:
115 mq

Anno:
2017

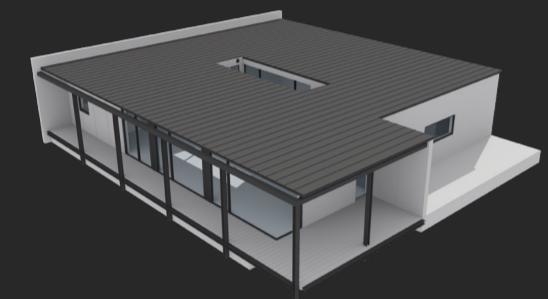

MASK HOUSE


La residenza si trova lungo un piccolo fiume, l'ingresso è infatti caratterizzato dalla presenza di un piccolo ponte e l'intera struttura è rialzata. Il progetto si contraddistingue nettamente con le abitazioni del complesso residenziale in cui è inserito. Il bianco dell'intonaco contrapposto alla struttura portante in acciaio scuro e il mattone sono usati tuttavia per inserire al meglio la Mask House nel contesto. La pedana lungo il corso d'acqua è realizzata facendo galleggiare il pavimento con acciaio. Data la sua esposizione ottimale la luce del sole può essere assicurata dalla mattina fino alla sera.



PROSPETTO EST



PROSPETTO OVEST

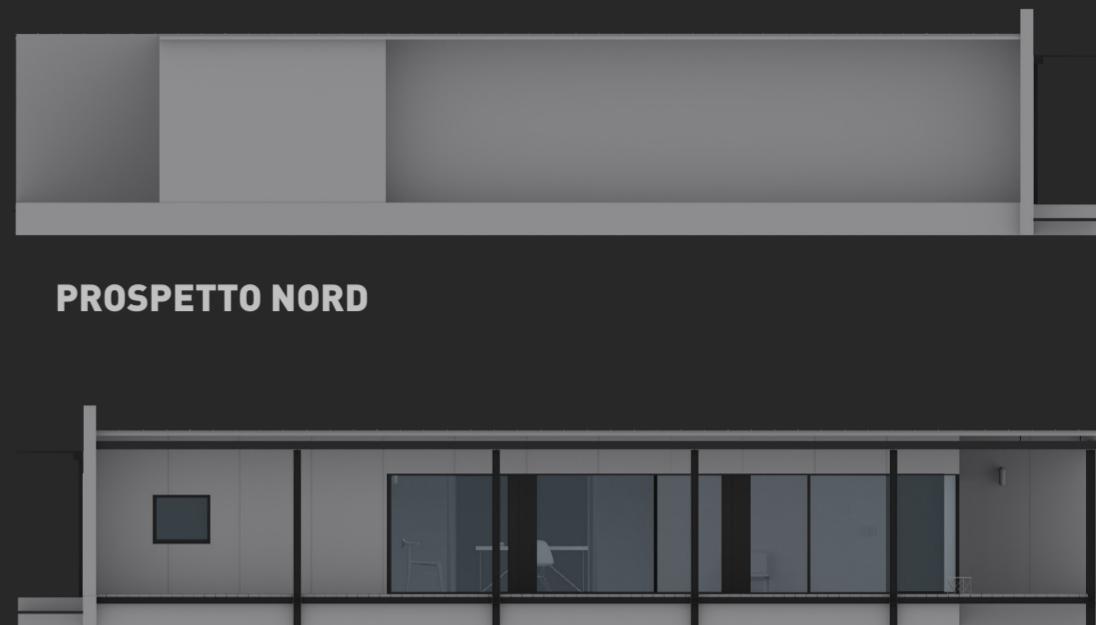



PROSPETTO NORD



PROSPETTO SUD



SEZIONE B - B'

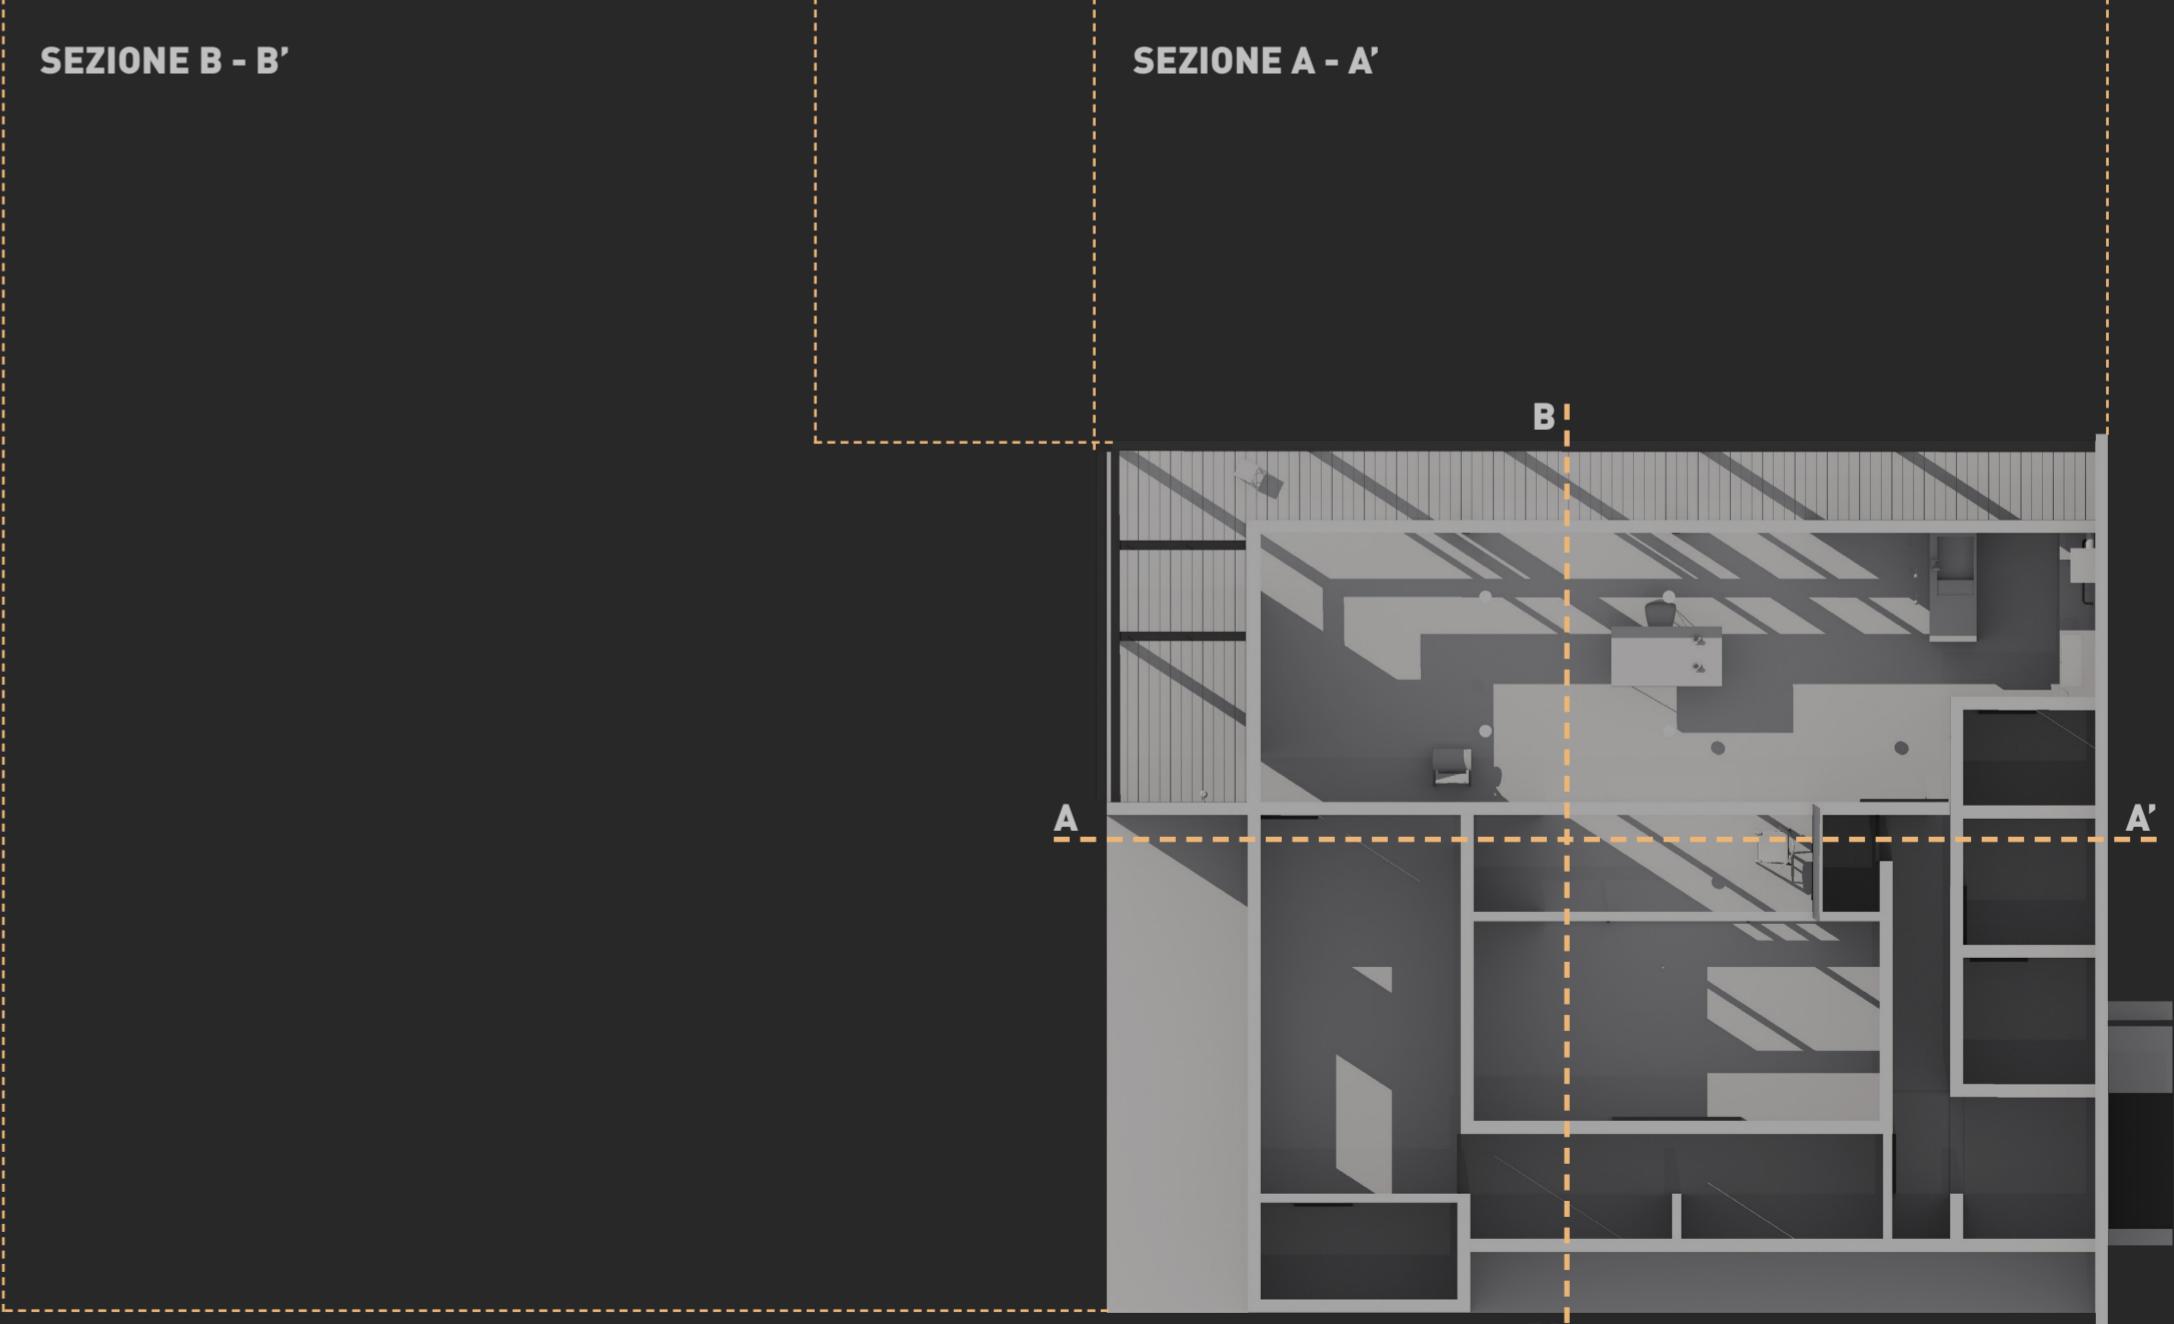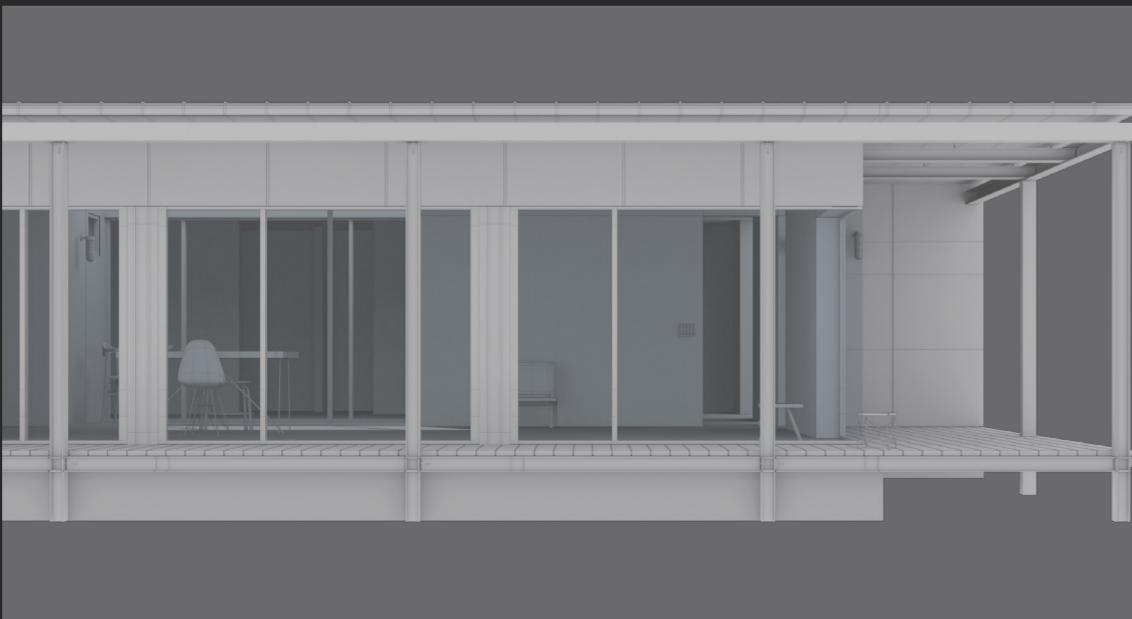

SEZIONE A - A'

